



PROJECT NAME: KSU Combs Hall 4 4
CLIENT: Wildcats Flooring

WILDCATS FLOORING

Date: 03/13/2024

SUMMARY OF TAKEOFFS

Type	Mark	Description	Model	QTY	Unit	Detailed QTY	Unit
FLOOR							
Vinyl	LVT1	LUXURY VINYL TILE	TARKETT EVENT STONE / URBAN STONE AVENUE SIZE: 12 BY 24 INCHES, VERTICAL ASHLAR.	11,062.00	SF	5,531.00	PCS
	LVT2	LUXURY VINYL TILE	TARKETT EVENT STONE / URBAN STONE MALIBU SIZE: 12 BY 24 INCHES, VERTICAL ASHLAR	8,924.00	SF	4,462.00	PCS
Resilient							
Resilient	RST1	RESILIENT STAIR TREADS	JOHNSONITE-TARKETT 86 HUNTER GREEN	552.00	SF	552.00	SF
	RSL1	RESILIENT STAIR LANDINGS	JOHNSONITE-TARKETT 86 HUNTER GREEN	552.00	SF	552.00	SF
Resinous							
Resinous	RSF1	RESINOUS FLOORING	SHERWIN WILLIAMS -- RIVER ROCK FLAKE SYSTEM	2,771.00	SF	2,771.00	SF
Concrete							
Concrete	CFC1	CONCRETE FLOOR COATING	SHERWIN WILLIAMS PIGMENTED	1,508.00	SF	1,508.00	SF
Terazzo							
Terazzo	TZ1	TERAZZO	TO BE DETERMINED WHITE	284.00	SF	284.00	SF
BASE							
Resilient	VWB1	RESILIENT WALL BASE	JOHNSONITE-TARKETT48 GREY SIZE: 4" COVE BASE IN COIL FORM	6,074.00	LF	6,074.00	LF
Resinous							
Resinous	RSFB1	RESINOUS FLOORING COVE BASE	SHERWIN WILLIAMS RIVER ROCK FLAKE SYSTEM	926.00	LF	926.00	LF
WALL							
Tile	CWT1	CERAMIC WALL TILE	AMERICAN OLEAN COLOR STORY ICE WHITE SIZE: 4 BY 12 INCHES	2,765.00	SF	8,295.00	PCS
	PWT1	PORCELAIN WALL TILE	ATLAS CONCORDE RIFT GRAVEL SIZE: 12 BY 24 INCHES	1,245.00	SF	623.00	PCS
TRANSITIONS							
Transitions	TR1	LVT/CFC	RESILIENT REDUCER STRIP	17.00	LF	17.00	LF
	TR2	LVT/RSF	ALUMINUM METAL EDGE TO BE MECHANICALLY FASTENED UNDER LUXURY VINYL TILE	36.00	LF	36.00	LF
	TR3	LVT/TZ	ALUMINUM METAL EDGE TO BE MECHANICALLY FASTENED UNDER LUXURY VINYL TILE	7.00	LF	7.00	LF
	MB	METAL EDGE	METAL EDGE BOTTOM OF WALL TILE	502.00	LF	502.00	LF
	MC	METAL EDGE	OUTSIDE CORNER METAL EDGE	104.00	LF	104.00	LF

Estimating Notes:


- QTY includes 8% wastage
- Considered the Metal Edges for the Tiles

INTERIOR GENERAL NOTES

- Reference A-001 for general plan notes. All notes may not apply to this sheet.
- A. Reference architectural ceiling plans for ceiling heights and bulkhead color designations. Paint all bulkheads HP-1 or P-1 unless specifically noted otherwise. Bulkheads that are flush with walls provide color to match adjacent wall color.
 - B. Paint new and existing interior hollow metal door frames HP-2 (Dark Gray). Provide caulk joint at floor level.
 - C. Do not paint exposed brick unless specifically noted otherwise.
 - D. Paint all exposed conduit piping, and associated assemblies to match adjacent paint finish. Applies to all new & existing to remain in areas of renovation or new construction.
 - E. Paint general walls HP-1 or P-1 (Neutral) unless specifically noted otherwise.
 - F. Wall Base
 1. Do not install vinyl wall base on interior brick unless specifically noted otherwise. Provide caulk joint at floor level.
 2. Provide vinyl wall base around all casework unless specifically noted otherwise.
 - G. Appliances and vending equipment are not provided in this contract.

INTERIOR FLOOR PLAN NOTES

#	NOTE
1	12 24 13 - PROVIDE MANUAL ROLLER SHADES FULL WIDTH AND HEIGHT OF WINDOW.
2	10 14 00 - PROVIDE EXIT SIGN TYPE E AT THIS LOCATION.
3	10 14 00 - PROVIDE LUXURY VINYL TILE (LVT) TO CONCRETE FLOORING COATING (CFC). REFERENCE DETAIL 3J-001.
4	FLOORING TRANSITION LUXURY VINYL TILE (LVT) TO RESINOUS FLOORING (RSF). REFERENCE DETAIL 3J-001.
5	PROVIDE LUXURY VINYL TILE (LVT) AT MAIN LANDING OF STAIRWELL LANDING.
6	09 67 23.17 - PROVIDE RESINOUS FLOORING FLOORING AND COVE ON EXISTING QUARRY TILES CURB IN BATH AREA.
7	09 67 23.17 - PROVIDE CONTINUOUS ADA RESINOUS FLOORING CURB. REFERENCE SPECIFICATION FOR CLARIFICATION.
8	09 65 13 - PROVIDE RESILIENT STAIR LANDING (RSL) AT INTERMEDIATE LANDINGS.
9	FLOORING TRANSITION LUXURY VINYL TILE (LVT) TO TERRAZZO (TZ). REFERENCE DETAIL 3J-001.
10	09 65 19 - DIRECTION OF LUXURY VINYL TILE THROUGHOUT ENTIRE BUILDING, EAST TO WEST DIRECTION IN VERTICAL ASHLAR INSTALLATION.
11	09 30 00 - PROVIDE CERAMIC WALL TILE (CWT-1) AROUND ENTIRE ROOM. REFERENCE 10J-201 FOR TYPICAL ELEVATION.
12	09 66 23 - PROVIDE TERRAZZO ZINC TRANSITIONS.

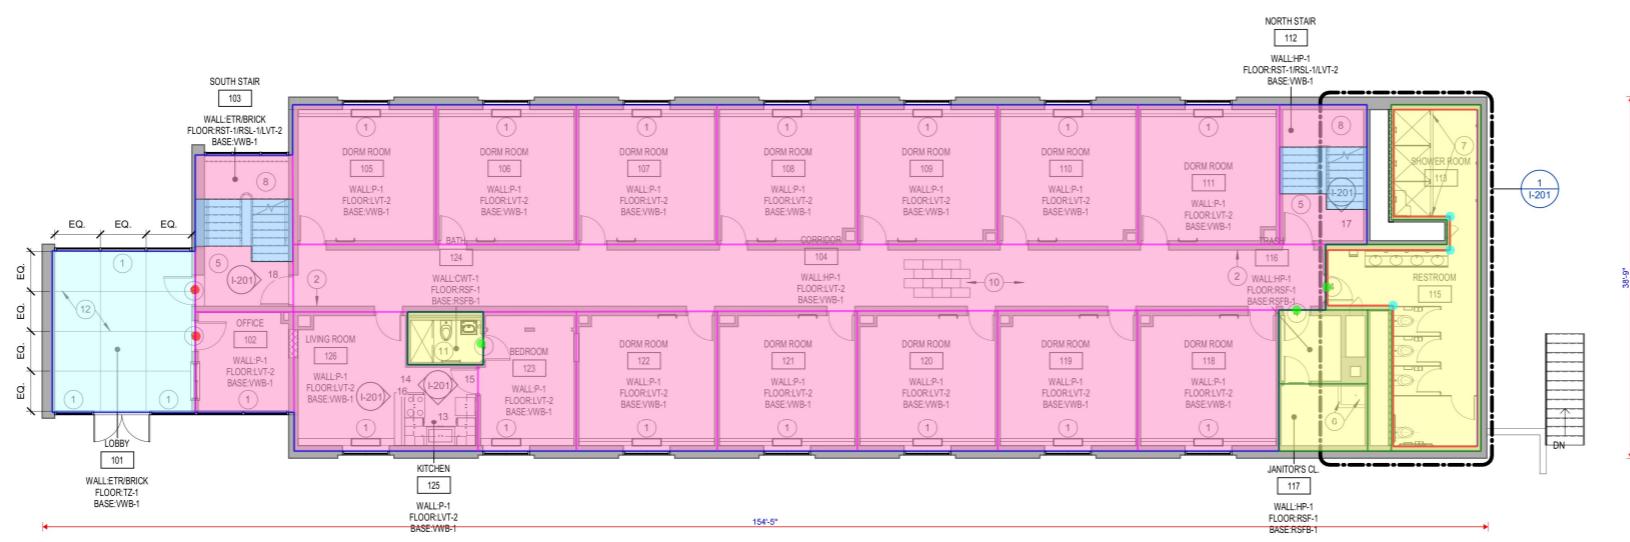

2 FIRST FLOOR INTERIOR PLAN

1/8" = 1'-0"

SPEC.	MARK	DESCRIPTION	MANUFACTURER	COLLECTION/PATTERN	COLOR	COMMENTS
08 14 16	WD	FLUSH WOOD DOORS	IVT INDUSTRIES	WHITE BIRCH	CLEAR CL18	
09 30 00	CWT-1	CERAMIC WALL TILE	AMERICAN OLEAN	COLOR STORY	ICE WHITE	SIZE: 4 BY 12 INCHES
09 30 00	PWT-1	PORCELAIN WALL TILE	ATLAS CONCORDE	RIFT	GRAVEL	SIZE: 12 BY 24 INCHES
09 65 13	RWB-1	RESILIENT WALL BASE	JOHNSONITE-TARKETT	--	48 GREY	SIZE: 4" COVE BASE IN COIL FORM.
09 65 13	RST-1	RESILIENT STAIR TREADS	JOHNSONITE-TARKETT	--	86 HUNTER GREEN	
09 65 13	RSL-1	RESILIENT STAIR LANDINGS	JOHNSONITE-TARKETT	--	86 HUNTER GREEN	
09 65 19	LVT-1	LUXURY VINYL TILE	TARKETT	EVENT STONE / URBAN STONE	AVENUE	SIZE: 12 BY 24 INCHES, VERTICAL ASHLAR
09 65 19	LVT-2	LUXURY VINYL TILE	TARKETT	EVENT STONE / URBAN STONE	MALIBU	SIZE: 12 BY 24 INCHES, VERTICAL ASHLAR
09 66 23	TZ-1	TERRAZZO	TO BE DETERMINED	--	WHITE	
09 67 23.13	CFC-1	CONCRETE FLOOR COATING (LEVEL 1)	SHERWIN WILLIAMS	--	PIGMENTED	
09 67 23.17	RSF-1	RESINOUS FLOORING COVE BASE	SHERWIN WILLIAMS	--	RIVER ROCK	FLAKE SYSTEM
09 67 23.17	RSF-1	RESINOUS FLOORING	SHERWIN WILLIAMS	--	RIVER ROCK	FLAKE SYSTEM
09 91 23.99	P-1	INTERIOR PAINTING	SHERWIN WILLIAMS	--	SW7015 REPOSE	GENERAL NEUTRAL GREY
09 91 23.99	P-2	INTERIOR PAINTING	SHERWIN WILLIAMS	--	SW7068 GRIZZLE	DARK GRAY
09 91 23.99	P-3	INTERIOR PAINTING	SHERWIN WILLIAMS	--	SW7007 CEILING BRIGHT WHITE	WHITE
09 91 23.99	TXP-1	INTERIOR PAINTING	SHERWIN WILLIAMS	--	SW7007 CEILING	WHITE TEXTURED CEILINGS
09 91 23.99	TXP-2	INTERIOR PAINTING	SHERWIN WILLIAMS	--	SW7068 GRIZZLE	GREY TEXTURED CEILINGS
09 96 00.99	HP-1	HIGH PERFORMANCE PAINT	SHERWIN WILLIAMS	--	SW7015 REPOSE	DARK GRAY
09 96 00.99	HP-2	HIGH PERFORMANCE PAINT	SHERWIN WILLIAMS	--	SW7068 GRIZZLE	DOOR FRAMES / STAIR RAILING
09 96 00.99	HP-3	HIGH PERFORMANCE PAINT	SHERWIN WILLIAMS	--	SW7007 CEILING	WHITE
12 32 00	PL-1	PLASTIC LAMINATE	WILSONART	--	467-36 STEEL MESH	CASEWORK
12 36 61.16	SS-1	SOLID SURFACE	WILSONART	--	9208CS WHITE STONE	

2063.3 SQ FT

4207.9 SQ FT

897.4 SQ FT

225.6 SQ FT

262.6 SQ FT

1395.7 SQ FT

802.8 FT

658.5 FT

294.1 FT

80.1 FT

36.1 FT


116.2 FT

5.0 EA

5.0 EA

2.0 EA

3.0 EA

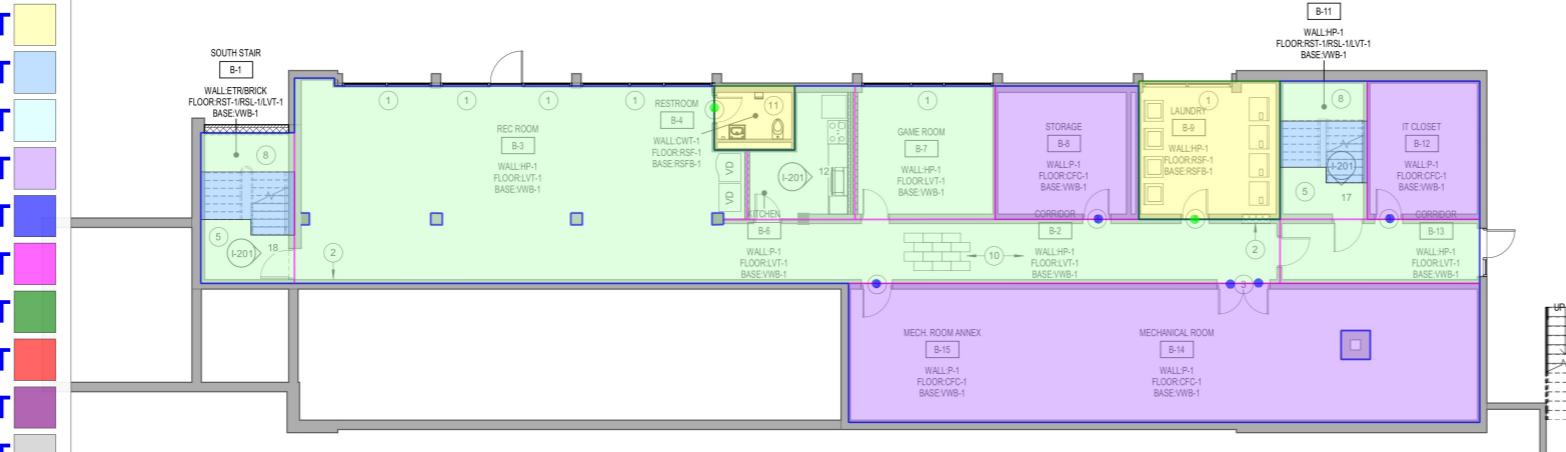

1 BASEMENT FLOOR INTERIOR PLAN

1/8" = 1'-0"

DRAWING INFORMATION		OVERALL INTERIOR PLANS		DRAWING NO. IN101
A & E FILE NO. 2023-109.COM		COMMONWEALTH OF KENTUCKY FINANCE AND ADMINISTRATION CABINET DEPARTMENT FOR FACILITIES AND SUPPORT SERVICES DIVISION OF ENGINEERING AND CONTRACT ADMINISTRATION FRANKFORT, KENTUCKY		
DRAWING DATE 02.12.2024		ENGR. FILE NO. #435-CB82-KS52-01		
DRAWN BY LAH		CHECKED BY LAH		
PHASE BID DOCUMENTS		RTA DATE 02.12.2024		
DECA REVIEWED		FOR INTENT ONLY		
SCHMIDT ASSOCIATES		DECA LOG #		
REVISED HISTORY OF THIS DRAWING				
#	DESCRIPTION OF REVISIONS	DATE	DESCRIPTION OF REVISIONS	
5				
6				
7				
8				


SARAH K. HEMPESTED
REGISTERED ARCHITECT
KENTUCKY
SCHMIDT ASSOCIATES

INTERIOR GENERAL NOTES	
Reference A-001 for general plan notes. All notes may not apply to this sheet.	
A.	Reference architectural ceiling plans for ceiling heights and bulkhead color designations. Paint all bulkheads HP-1 or P-1 unless specifically noted otherwise. Bulkheads that are flush with walls provide color to match adjacent wall color.
B.	Paint new and existing interior hollow metal door frames HP-2 (Dark Gray).
C.	Do not paint exposed brick unless specifically noted otherwise.
D.	Paint all exposed conduit piping, and associated assemblies to match adjacent paint finish. Applies to all new & existing to remain in areas of renovation or new construction.
E.	Paint general walls HP-1 or P-1 (Neutral) unless specifically noted otherwise.
F.	Wall Base 1. Do not install vinyl wall base on interior brick unless specifically noted otherwise. Provide caulk joint at floor level. 2. Provide vinyl wall base around all casework unless specifically noted otherwise.
G.	Appliances and vending equipment are not provided in this contract.



3 FOURTH FLOOR INTERIOR PLAN
1/8" = 1'-0"

#	NOTE
1	12 24 13 - PROVIDE MANUAL ROLLER SHADES FULL WIDTH AND HEIGHT OF WINDOW.
2	10 14 00 - PROVIDE EXIT SIGN TYPE E AT THIS LOCATION.
3	10 14 00 - PROVIDE LUXURY VINYL TILE (LVT) TO CONCRETE FLOORING COATING (CFC). REFERENCE DETAIL 2J-001.
4	FLOORING TRANSITION LUXURY VINYL TILE (LVT) TO RESINOUS FLOORING (RSF). REFERENCE DETAIL 2J-001.
5	PROVIDE LUXURY VINYL TILE (LVT) AT MAIN LANDING OF STAIRWELL LANDING.
6	09 67 23.17 - PROVIDE RESINOUS FLOORING FLOORING AND COVE ON EXISTING QUARRY TILED CURVE IN HALL AREA.
7	09 67 23.17 - PROVIDE CONTINUOUS ADA RESINOUS FLOORING CURB. REFERENCE SPECIFICATION FOR CLARIFICATION.
8	09 65 13 - PROVIDE RESILIENT STAIR LANDING (RSL) AT INTERMEDIATE LANDINGS.
9	09 65 19 - DIRECTION OF LUXURY VINYL TILE (LVT) TO TERRAZZO (TZ). REFERENCE DETAIL 3J-001.
10	09 65 19 - DIRECTION OF LUXURY VINYL TILE THROUGHOUT ENTIRE BUILDING, EAST TO WEST DIRECTION IN VERTICAL ASHLAR INSTALLATION.
11	09 30 00 - PROVIDE CERAMIC WALL TILE (CWT-1) AROUND ENTIRE ROOM. REFERENCE 10J-201 FOR TYPICAL ELEVATION.
12	09 66 23 - PROVIDE TERRAZZO ZINC TRANSITIONS.

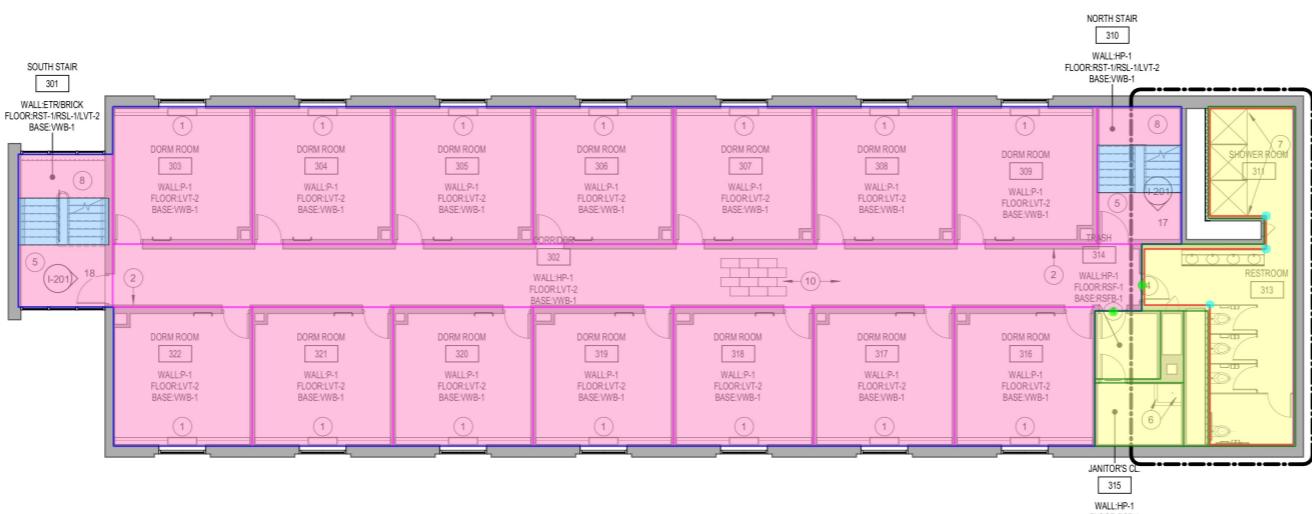

2 THIRD FLOOR INTERIOR PLAN
1/8" = 1'-0"



1 SECOND FLOOR INTERIOR PLAN
1/8" = 1'-0"

INTERIOR FINISH LEGEND						
SPEC.	MARK	DESCRIPTION	MANUFACTURER	COLLECTION/PATTERN	COLOR	COMMENTS
08 14 16	WD	FLUSH WOOD DOORS	IVT INDUSTRIES	WHITE BIRCH	CLEAR CL18	
09 30 00	CWT-1	CERAMIC WALL TILE	AMERICAN OLEAN	COLOR STORY	ICE WHITE	SIZE: 4 BY 12 INCHES
09 30 00	PWT-1	PORCELAIN WALL TILE	ATLAS CONCORDE	RIFT	GRAVEL	SIZE: 12 BY 24 INCHES
09 65 13	RWB-1	RESILIENT WALL BASE	JOHNSONITE-TARKETT	--	48 GREY	SIZE: 4" COVE BASE IN COIL FORM.
09 65 13	RST-1	RESILIENT STAIR TREADS	JOHNSONITE-TARKETT	--	86 HUNTER GREEN	
09 65 13	RSL-1	RESILIENT STAIR LANDINGS	JOHNSONITE-TARKETT	--	86 HUNTER GREEN	
09 65 19	LVT-1	LUXURY VINYL TILE	TARKETT	EVENT STONE / URBAN STONE	AVENUE	SIZE: 12 BY 24 INCHES, VERTICAL ASHLAR
09 65 19	LVT-2	LUXURY VINYL TILE	TARKETT	EVENT STONE / URBAN STONE	MALIBU	SIZE: 12 BY 24 INCHES, VERTICAL ASHLAR
09 66 23	TZ-1	TERRAZZO	TO BE DETERMINED	--	WHITE	
09 67 23.13	CFC-1	CONCRETE FLOOR COATING (LEVEL 1)	SHERWIN WILLIAMS	--	PIGMENTED	
09 67 23.17	RSF-1	RESINOUS FLOORING COVE BASE	SHERWIN WILLIAMS	--	RIVER ROCK	FLAKE SYSTEM
09 67 23.17	RSF-1	RESINOUS FLOORING	SHERWIN WILLIAMS	--	RIVER ROCK	FLAKE SYSTEM
09 91 23.99	P-1	INTERIOR PAINTING	SHERWIN WILLIAMS	SW7015 REPOSE	GENERAL NEUTRAL GREY	
09 91 23.99	P-2	INTERIOR PAINTING	SHERWIN WILLIAMS	SW7068 GRIZZLE	DARK GRAY	
09 91 23.99	P-3	INTERIOR PAINTING	SHERWIN WILLIAMS	SW7007 CEILING BRIGHT WHITE	WHITE	
09 91 23.99	TXP-1	INTERIOR PAINTING	SHERWIN WILLIAMS	SW7007 CEILING BRIGHT WHITE	WHITE TEXTURED CEILINGS	
09 91 23.99	TXP-2	INTERIOR PAINTING	SHERWIN WILLIAMS	SW7068 GRIZZLE	GREY TEXTURED COCO	
09 96 00.99	HP-1	HIGH PERFORMANCE PAINT	SHERWIN WILLIAMS	SW7015 REPOSE GREY	GENERAL NEUTRAL GREY	
09 96 00.99	HP-2	HIGH PERFORMANCE PAINT	SHERWIN WILLIAMS	SW7068 GRIZZLE GRAY	DOOR FRAMES / STAIR RAILING	
09 96 00.99	HP-3	HIGH PERFORMANCE PAINT	SHERWIN WILLIAMS	SW7007 CEILING WHITE	WHITE	
12 32 00	PL-1	PLASTIC LAMINATE	WILSONART	467-36 STEEL MESH	CASEWORK	
12 36 61.16	SS-1	SOLID SURFACE	WILSONART	9208CS WHITE STONE		

DRAWING INFORMATION		OVERALL INTERIOR PLANS		DRAWING NO. IN102
A & E FILE NO.	2023-109.COM	DRAWING DATE	02.12.2024	
DRAWN BY	LAH	CHECKED BY	LAH	
PHASE	BID DOCUMENTS	RTA DATE	02.12.2024	
REVISION HISTORY OF THIS DRAWING				
#	DESCRIPTION OF REVISIONS	DATE	DESCRIPTION OF REVISIONS	DATE
5				
6				
7				
8				

Sarah K. H. Schmidt, RA, LEED AP

SARAH K. HEMPESTED
REGISTERED ARCHITECT
COMM. OF KENTUCKY
NO. 8688
SCHMIDT ASSOCIATES
400 E Main Street Frankfort, KY 40601
730 Main Street, Suite 2000 Louisville, KY 40202
schmidt@schmidt.com